Dental Clinic Interior Design

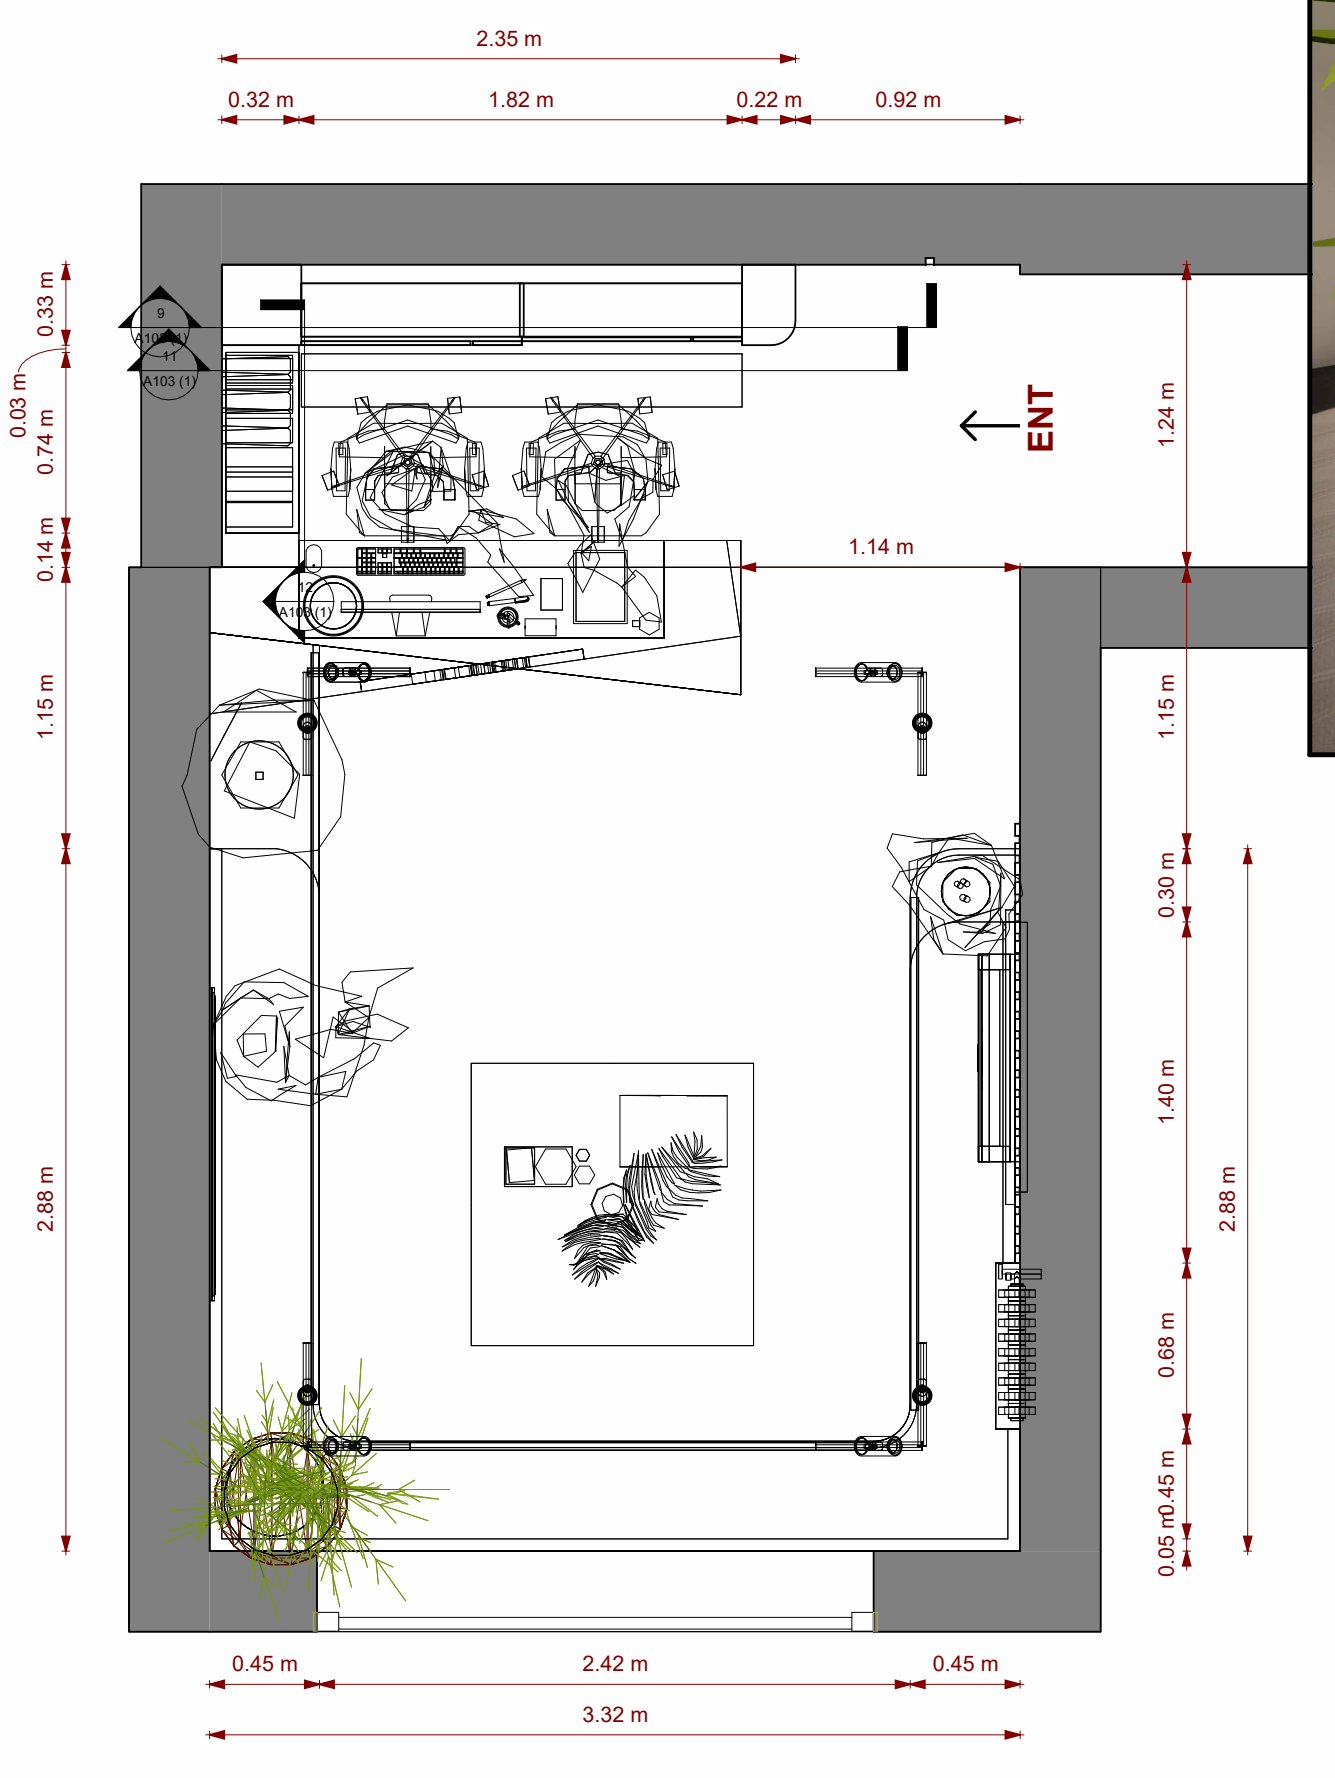

7 plan sheet
1 : 20

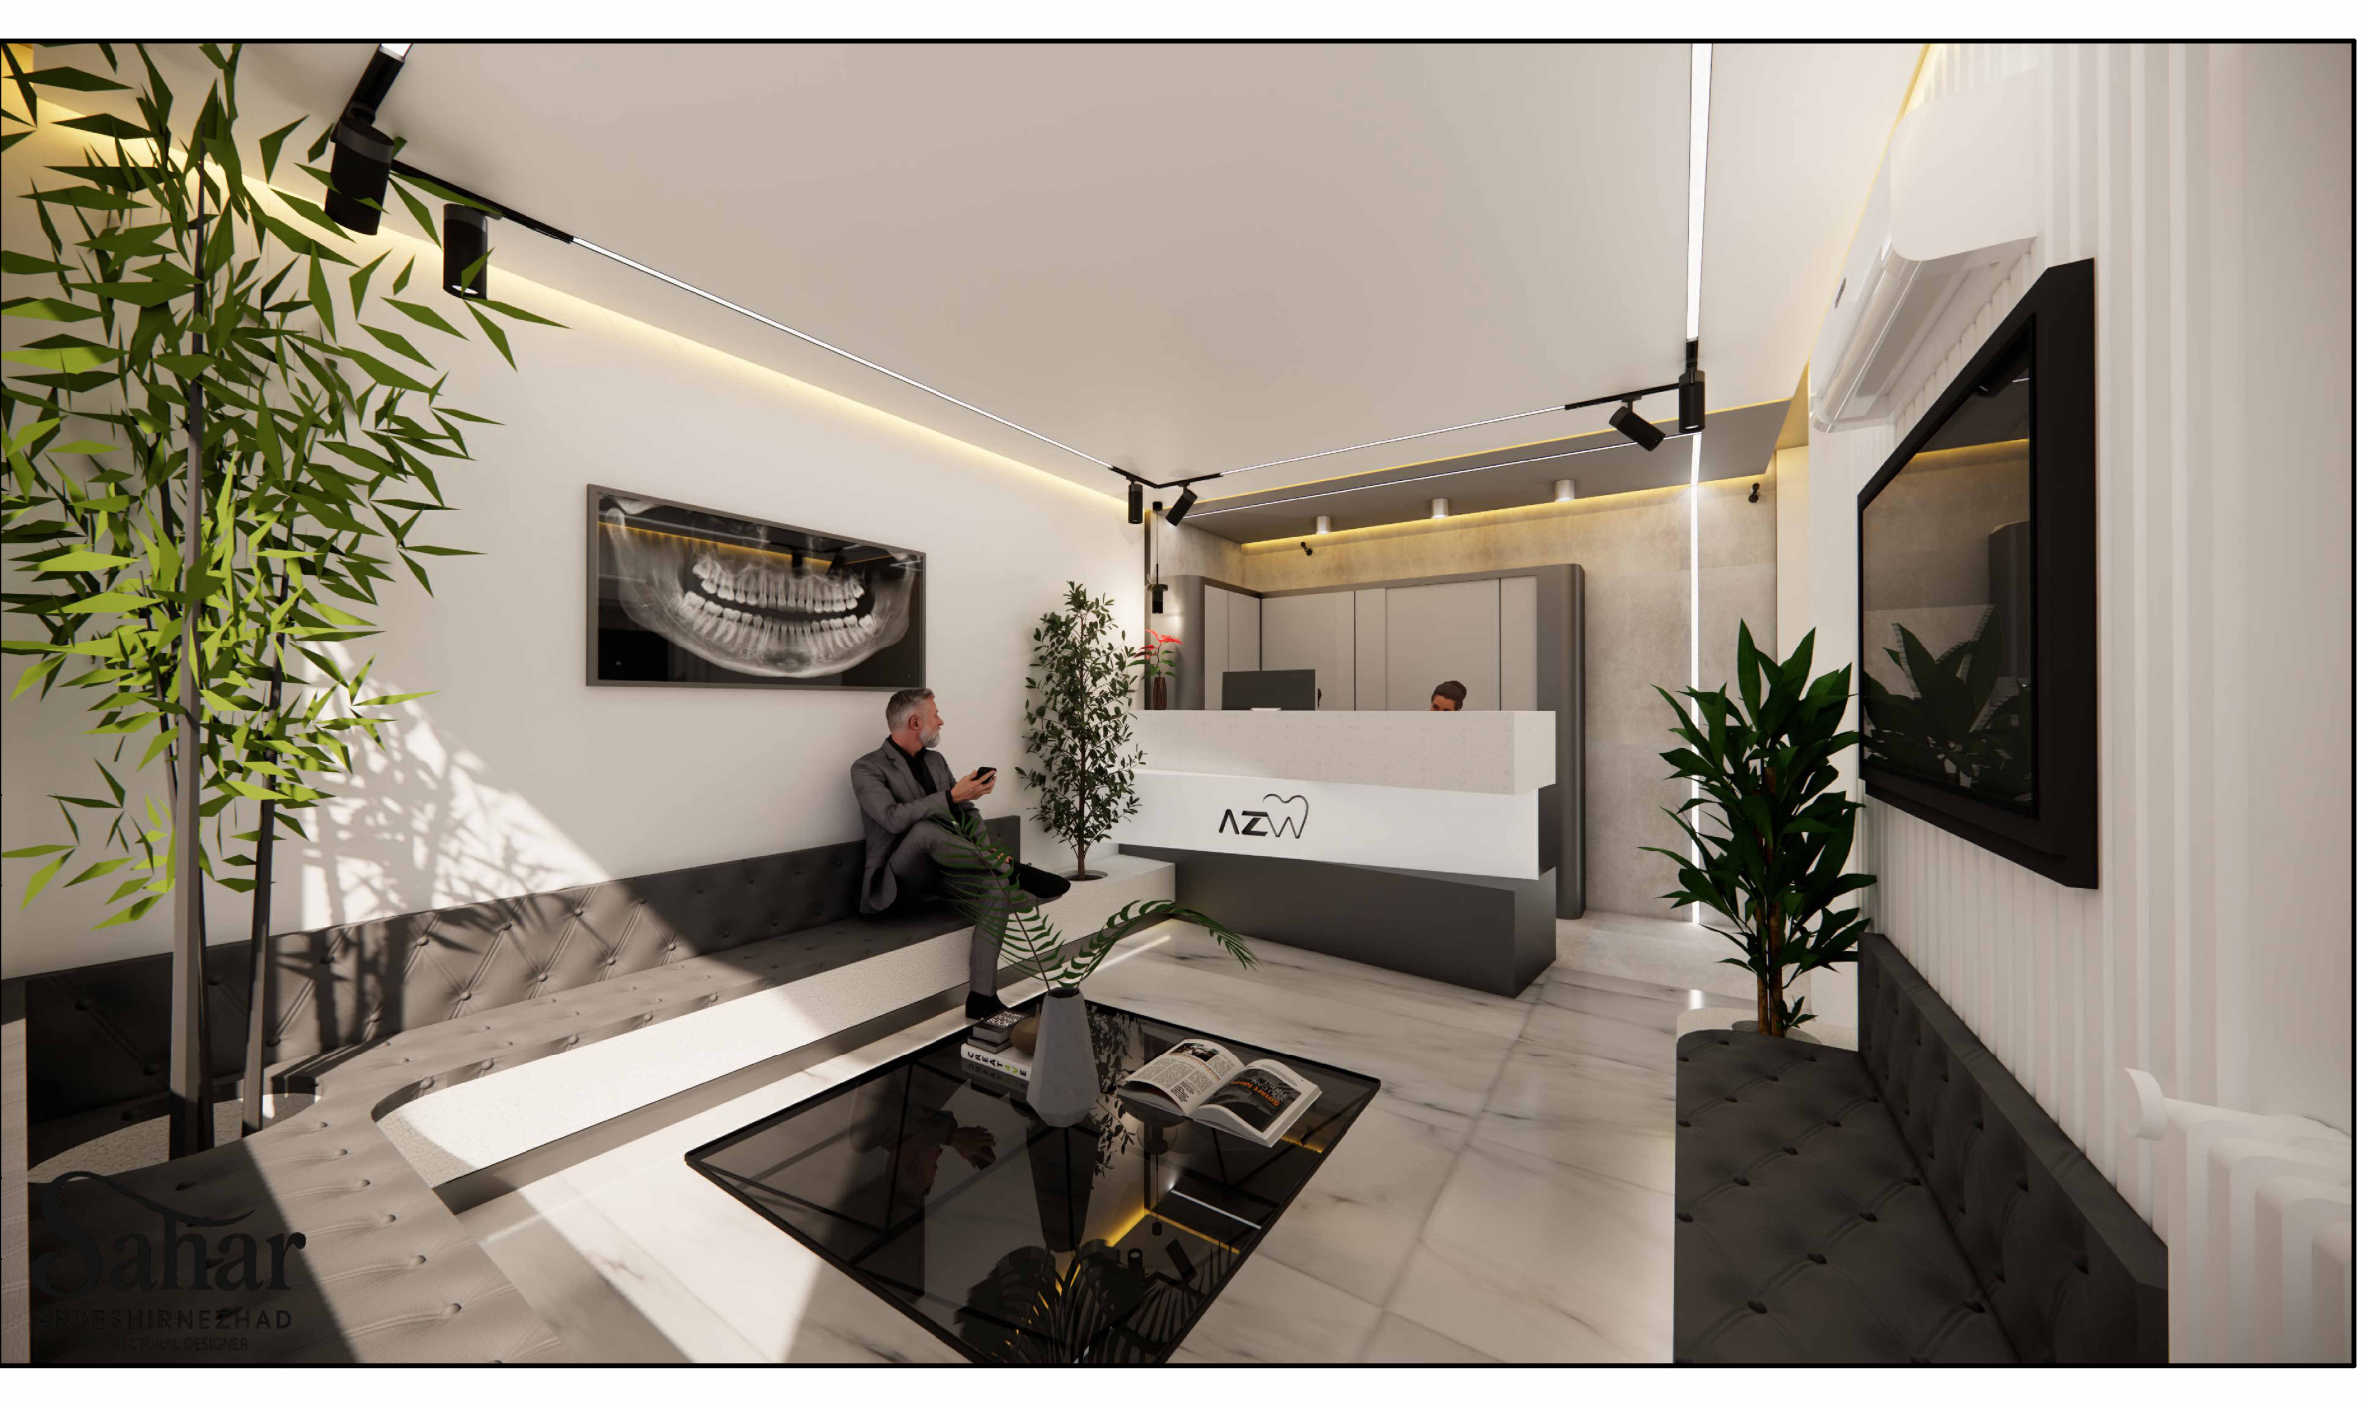

Where functionality meets contemporary elegance

Sahar
ARDESHIRNEZHAD
ARCHITECTURAL DESIGNER

A welcoming reception space designed to enhance patient comfort and create a professional first impression.

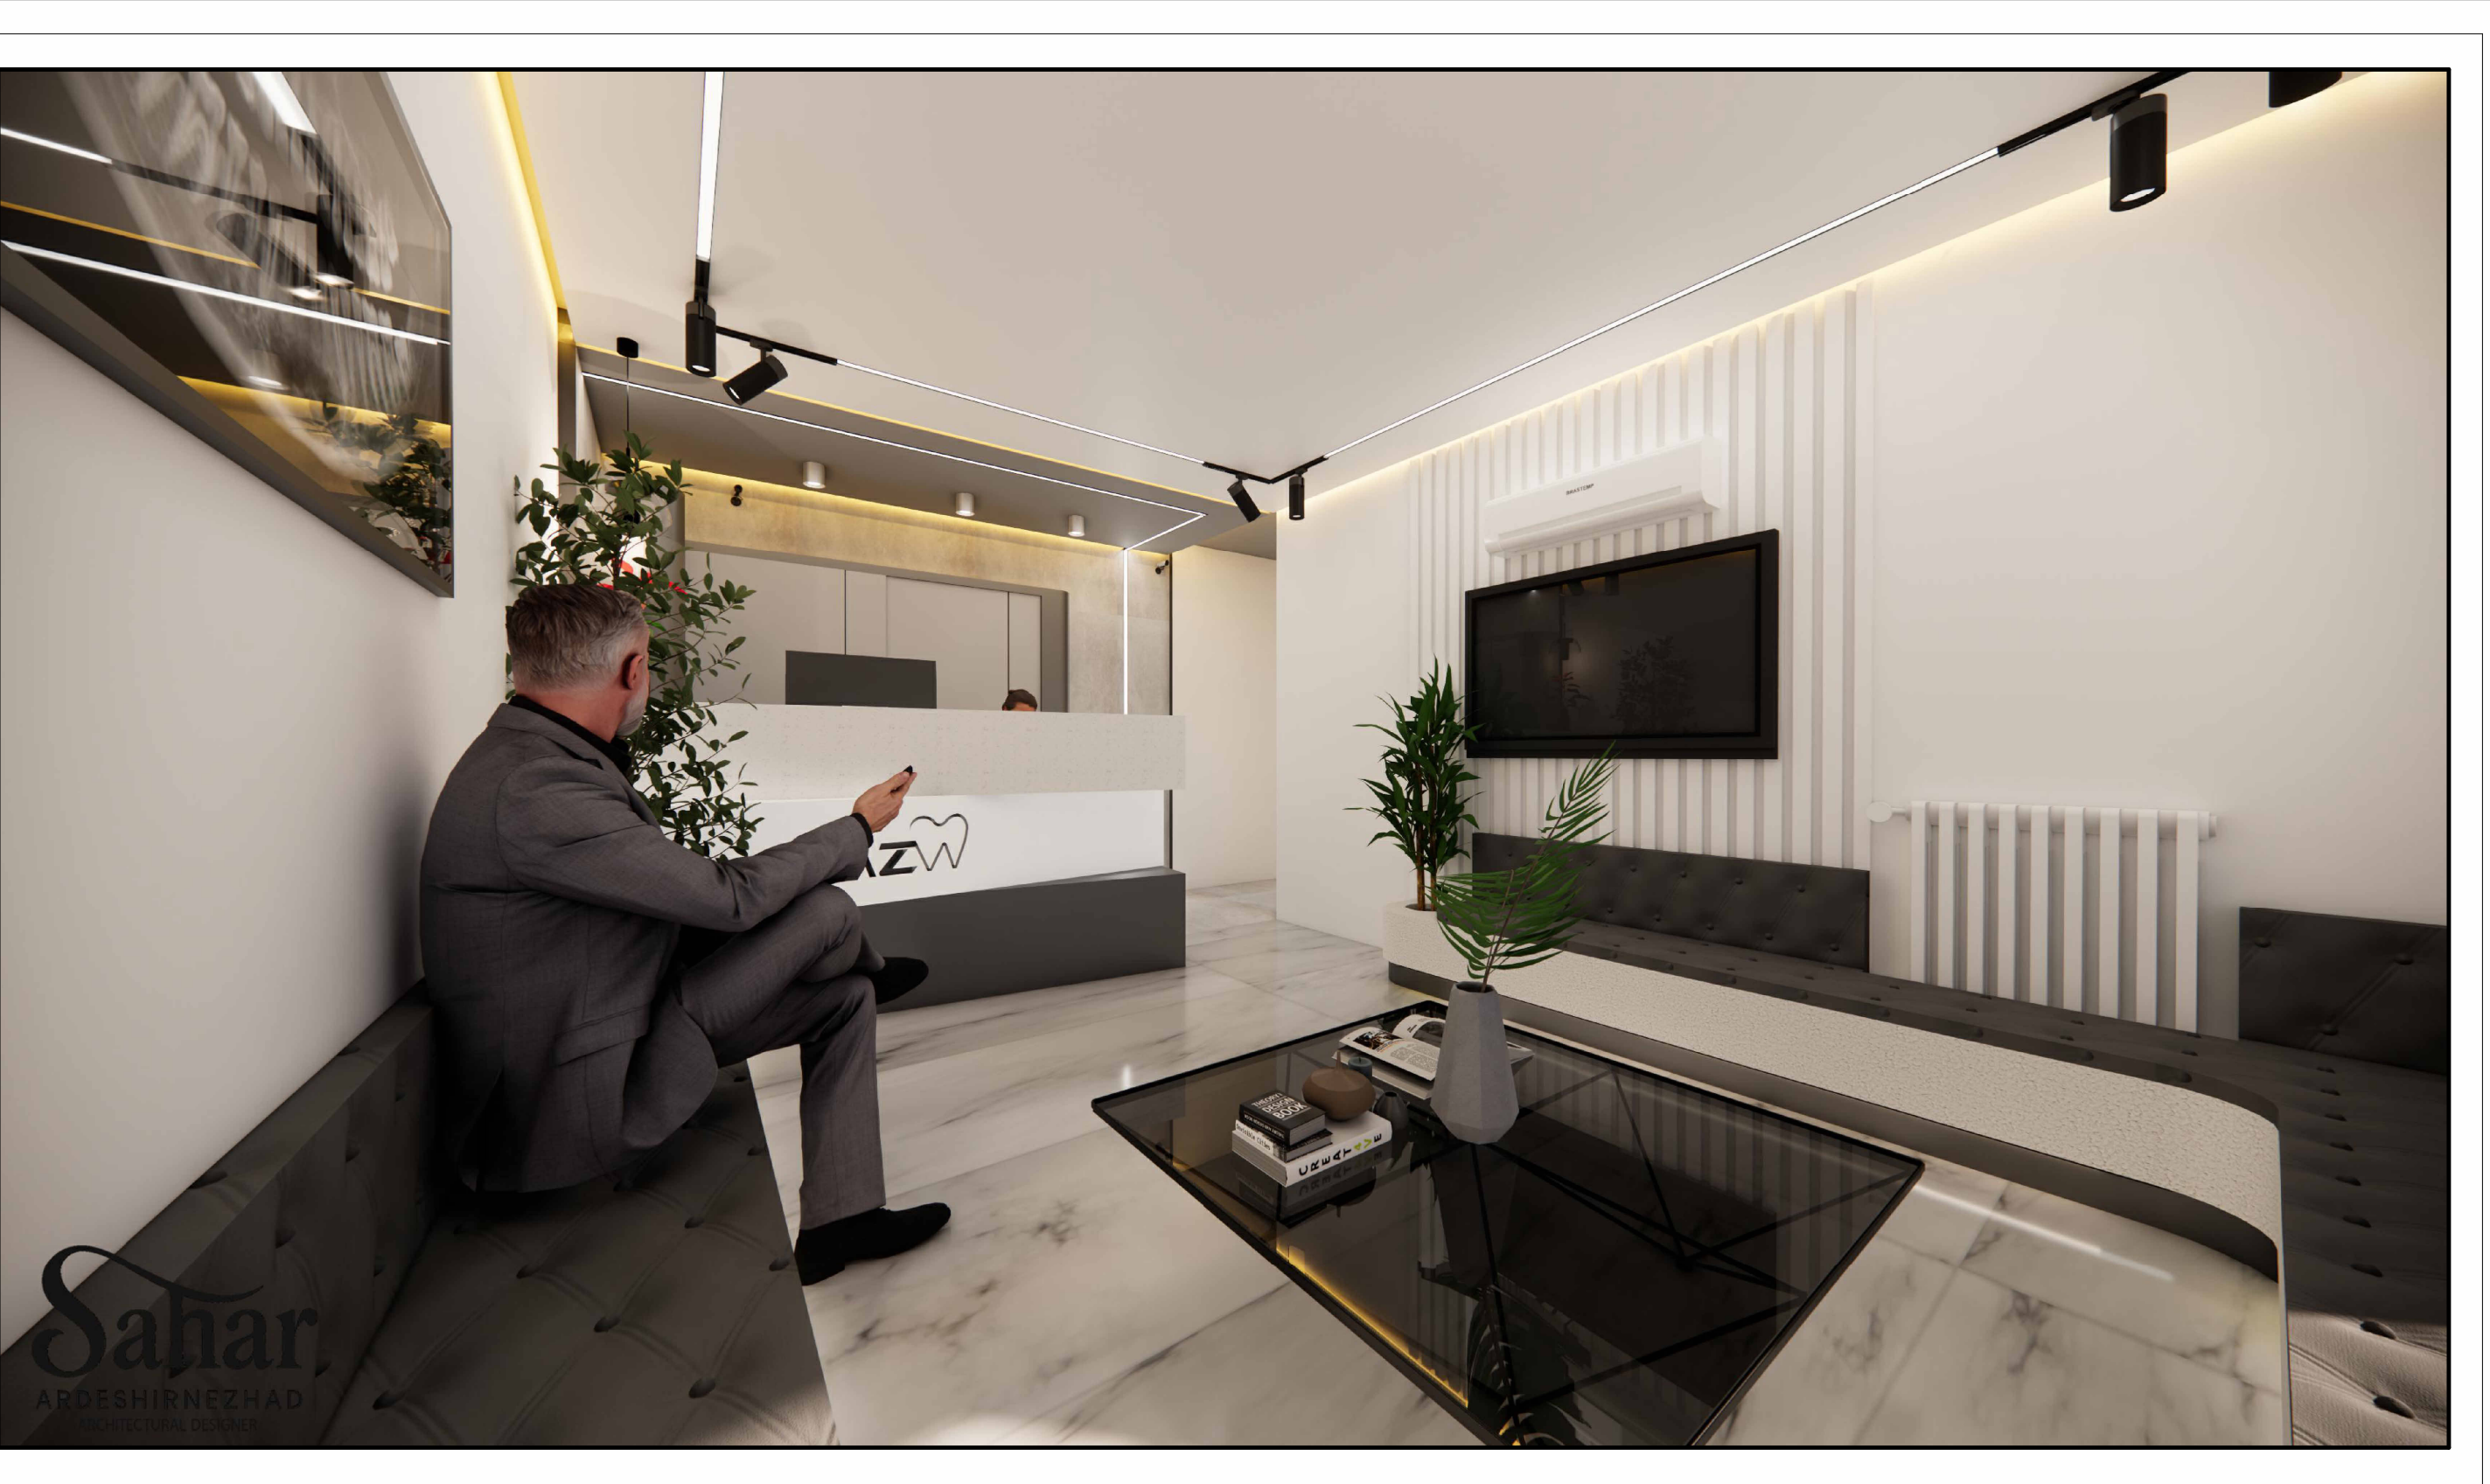

Sahar
ARDESHIRNEZHAD
ARCHITECTURAL DESIGNER

Clean lines, soft lighting, and timeless materials create a welcoming healthcare experience.

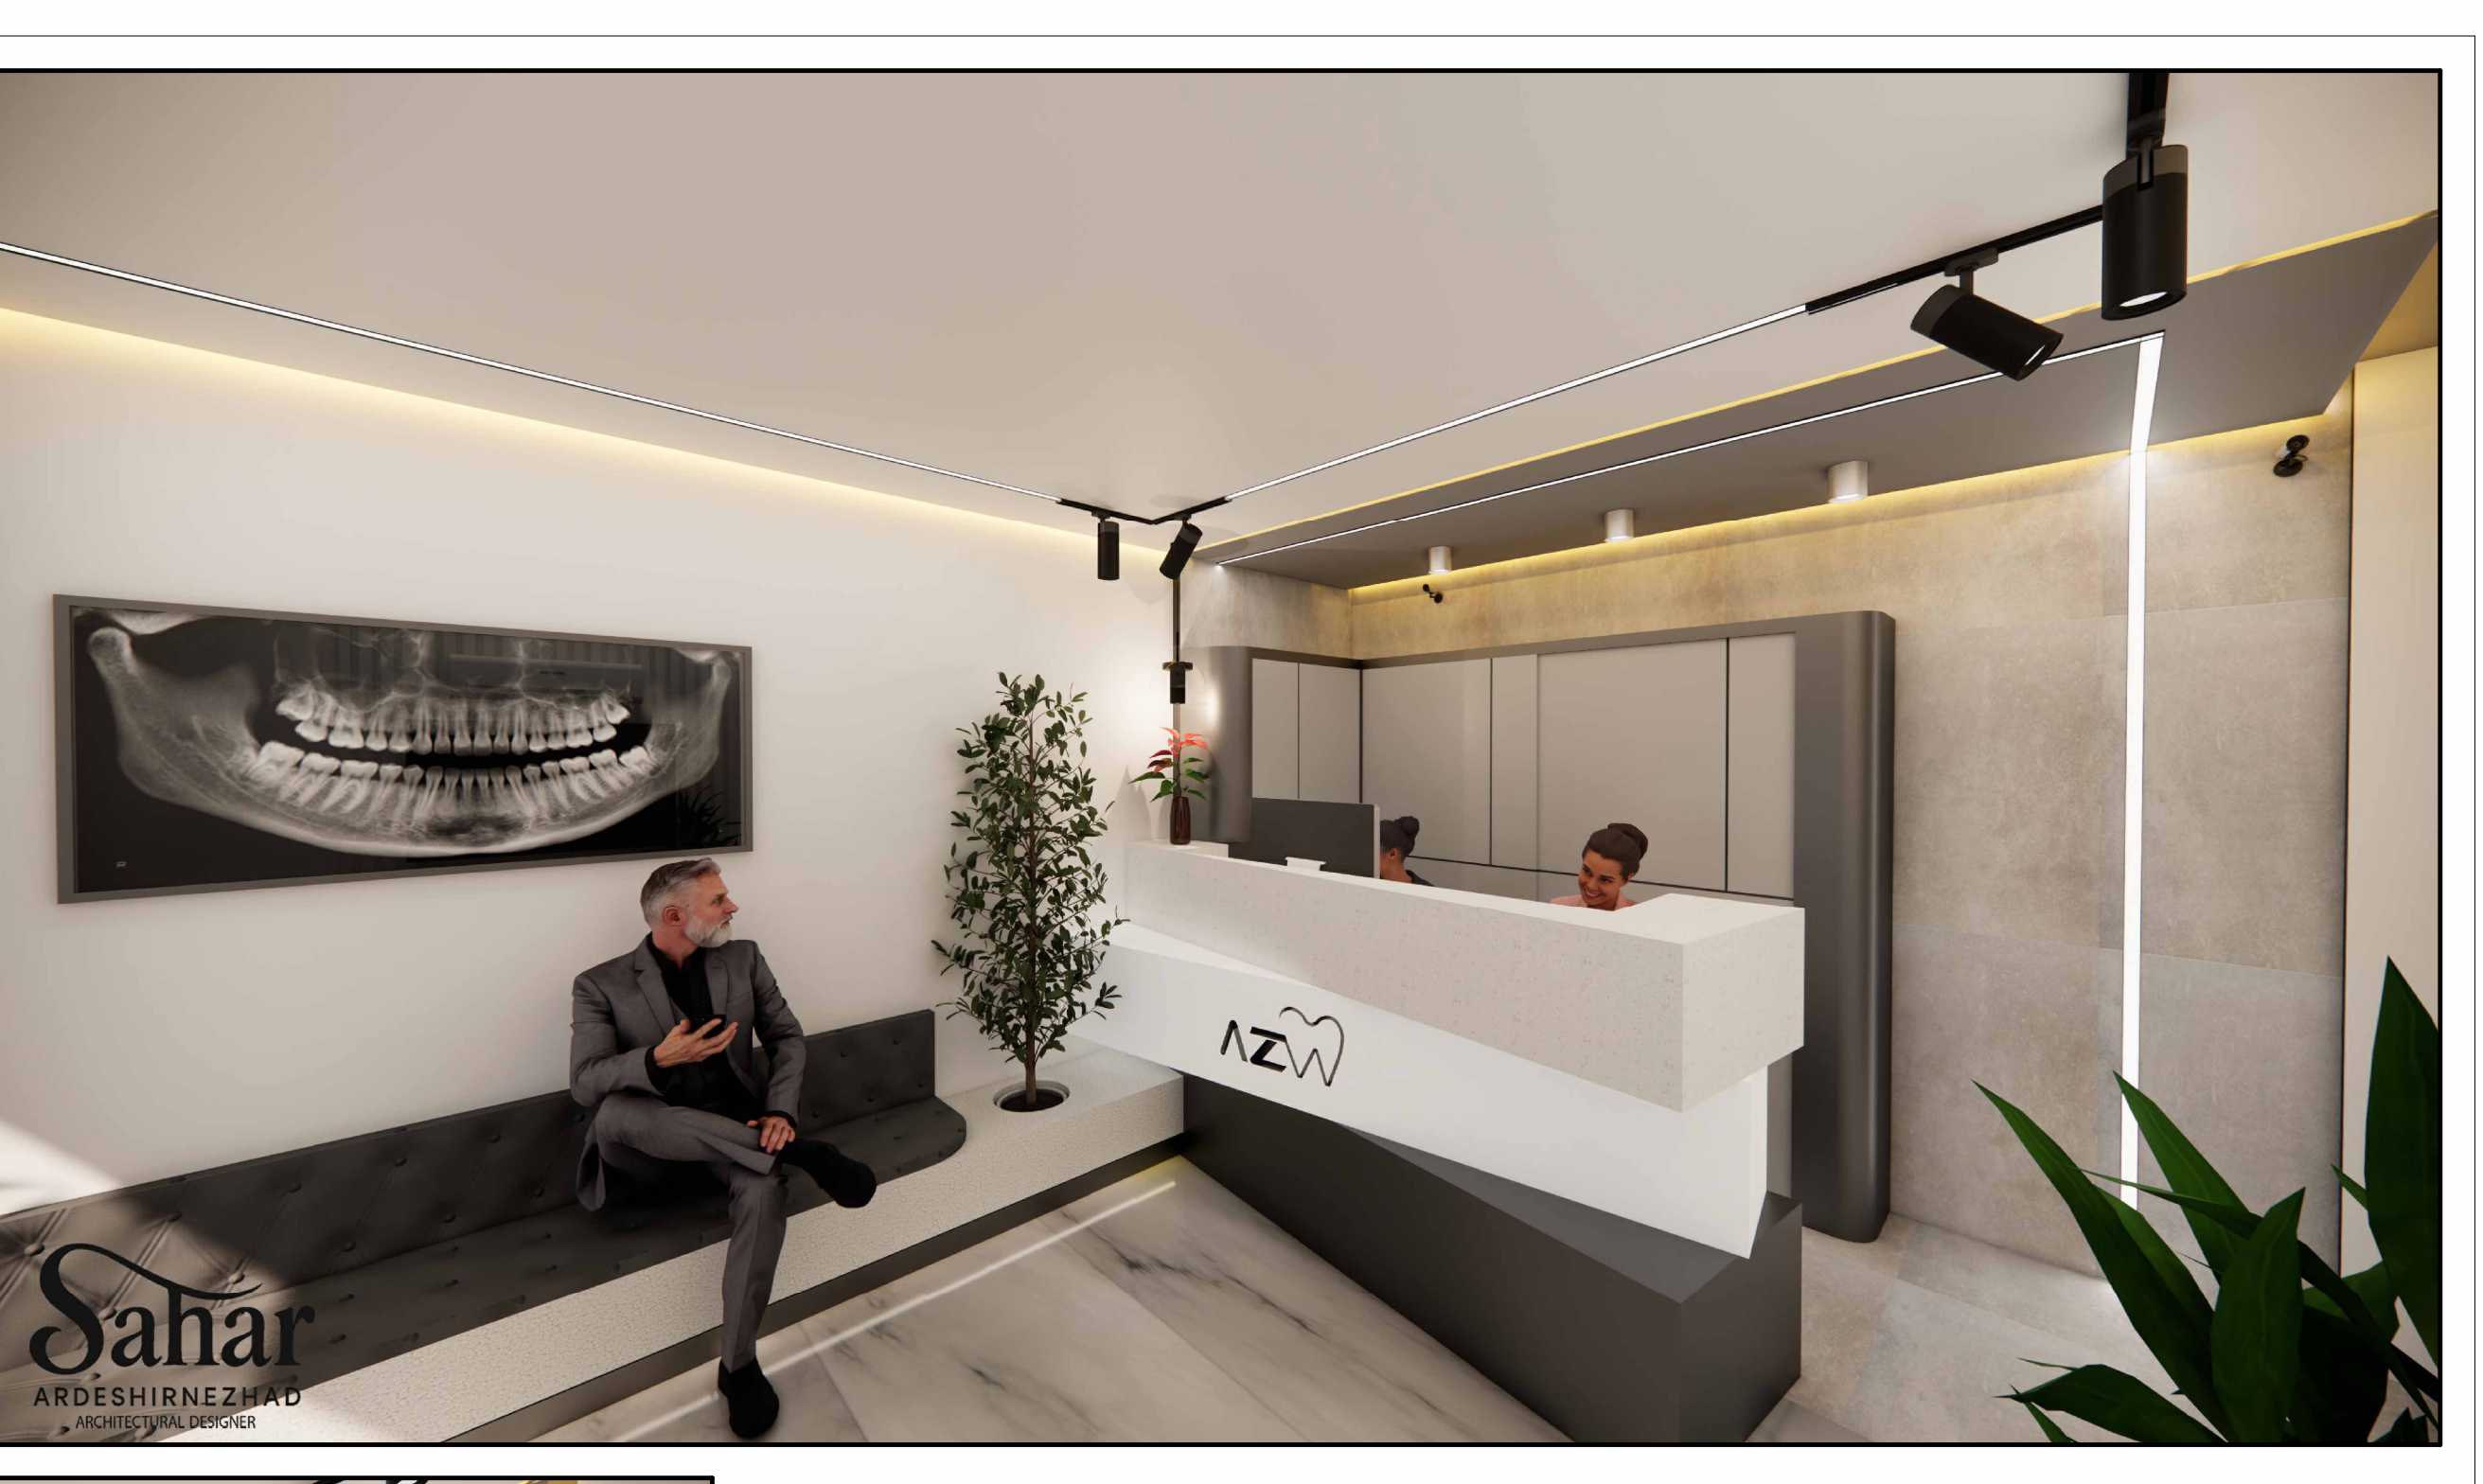

Modern Dental Care Center

Sahar
ARDESHIRNEZHAD
ARCHITECTURAL DESIGNER

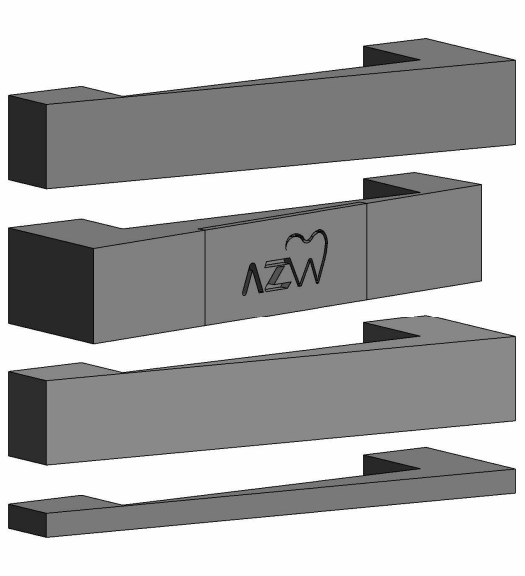

2 3d kanter Copy 1

مشخصات اجرا:

- اسکلت فلزی با پروفیل سنگین60*40میلی متر یا 30*60
- جوشکاری کامل و رنگ ضدزنگ
- اتصال پیچ و مهره با جوش
- سنگ کوارتز با چسب مخصوص سنگ
- نور مخفی با نوار ال ای دی24ولت
- پلکسی سفید10میلی متر ضخامت
- ام دی اف با رنگ طوسی تیره مات

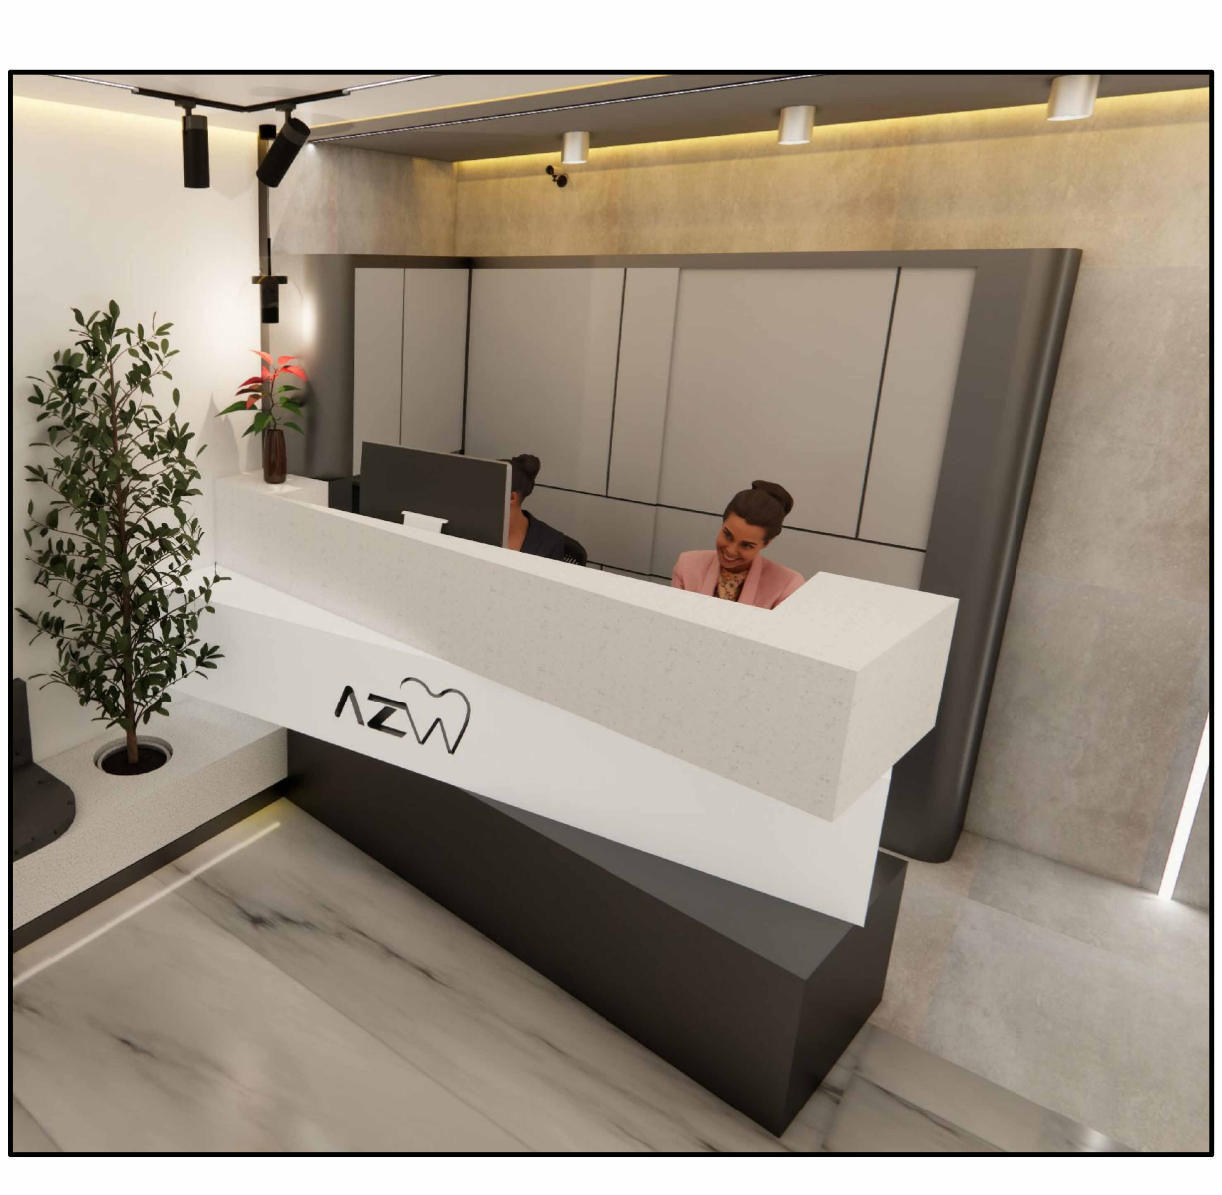

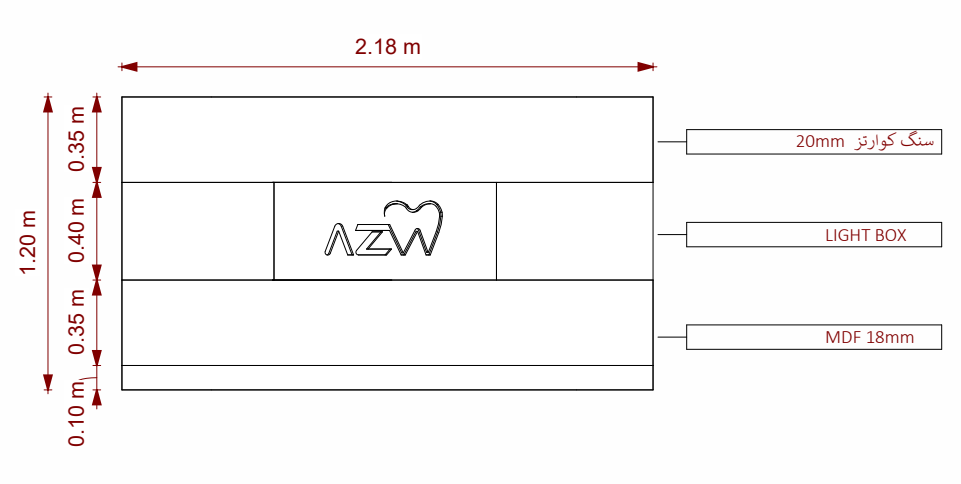

3 Section 1 - Dependent 1
1 : 20

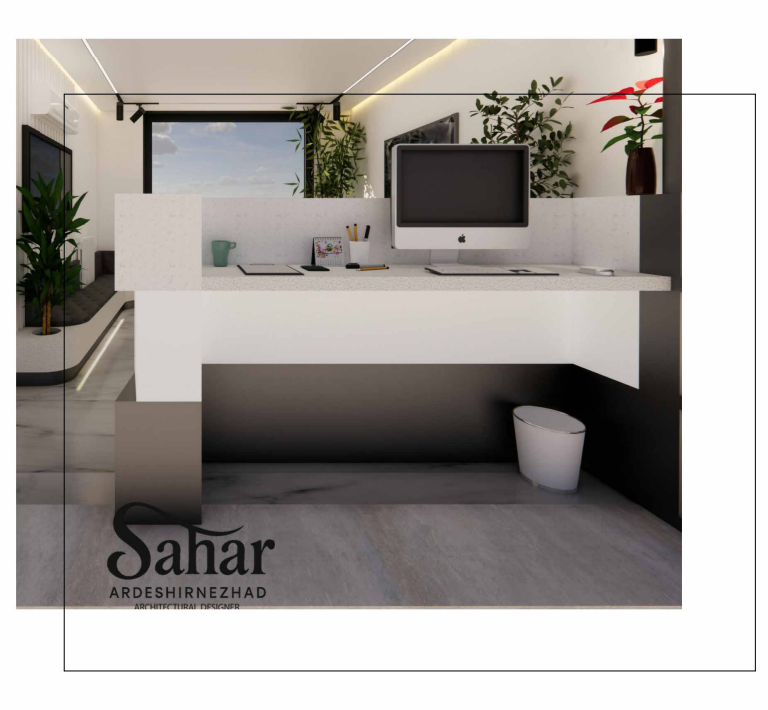

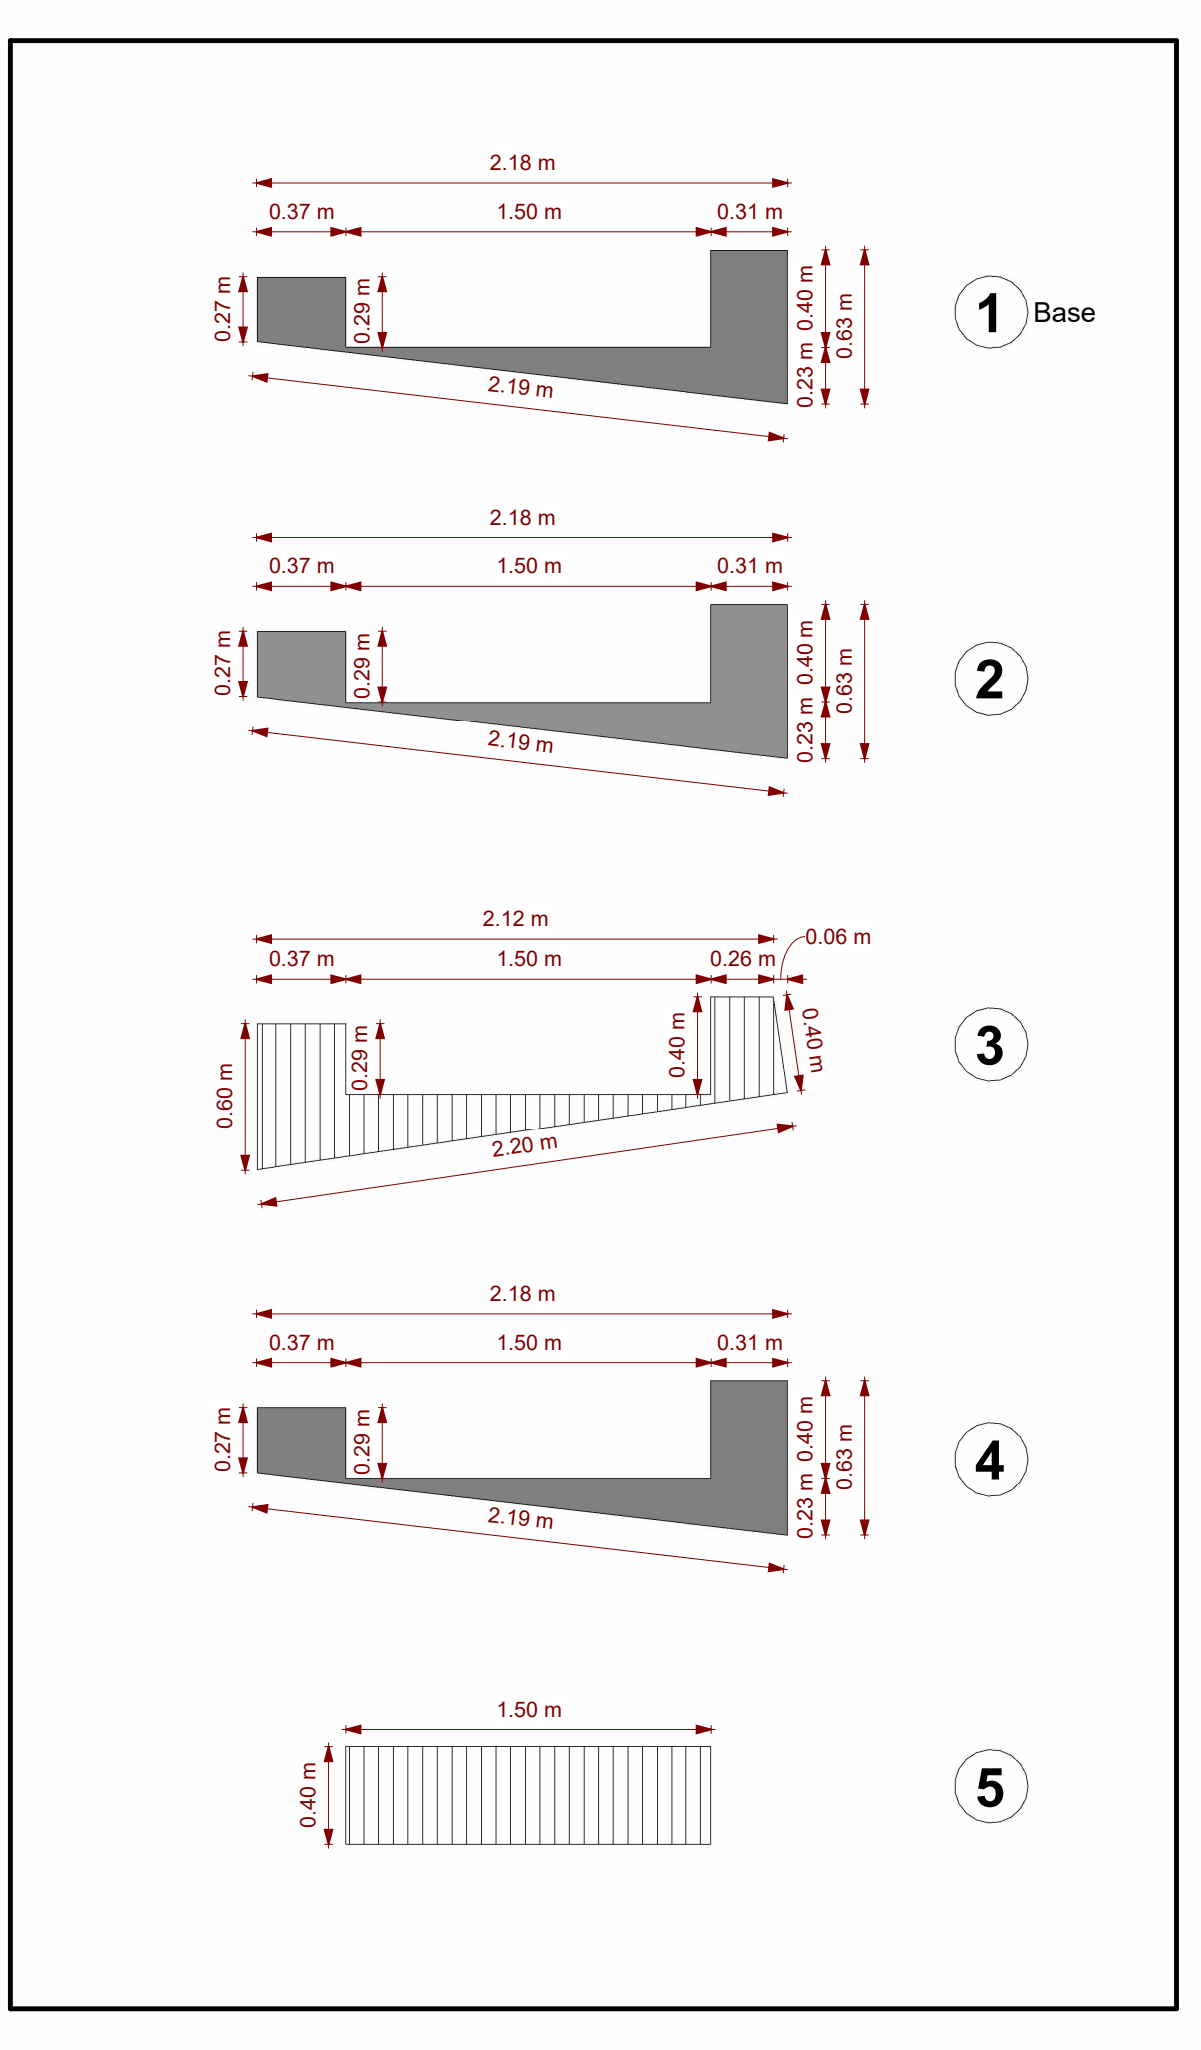

1 DIMENTION - Dependent 1
1 : 20

Sahar
ARDESHIRNEZHAD
ARCHITECTURAL DESIGNER

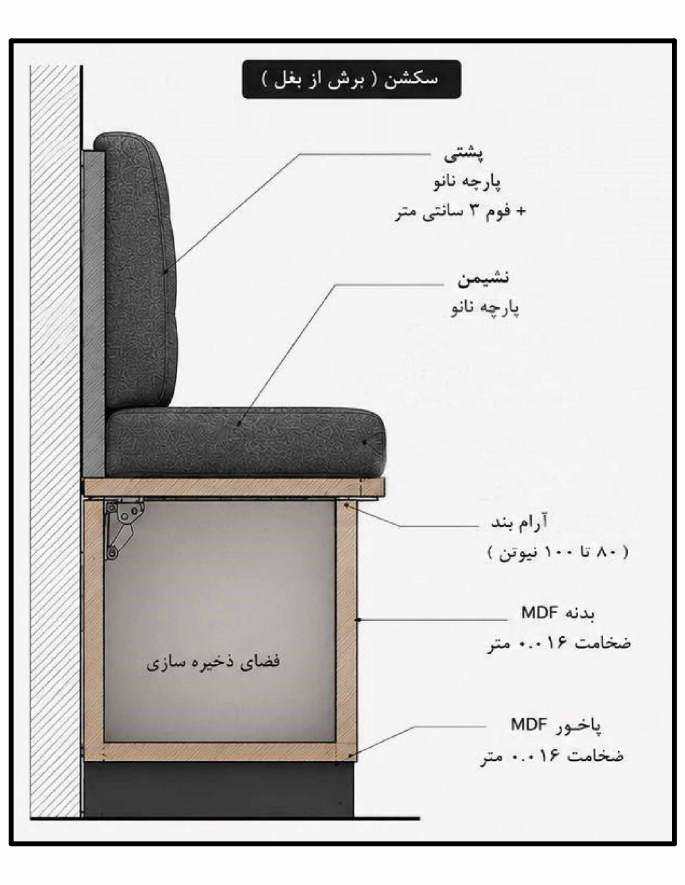

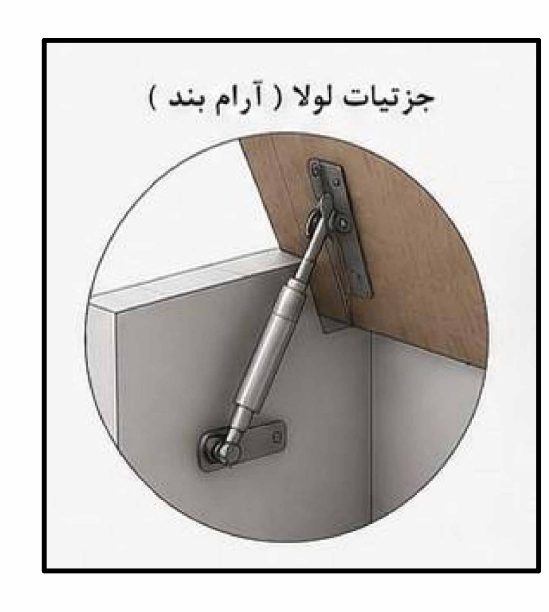

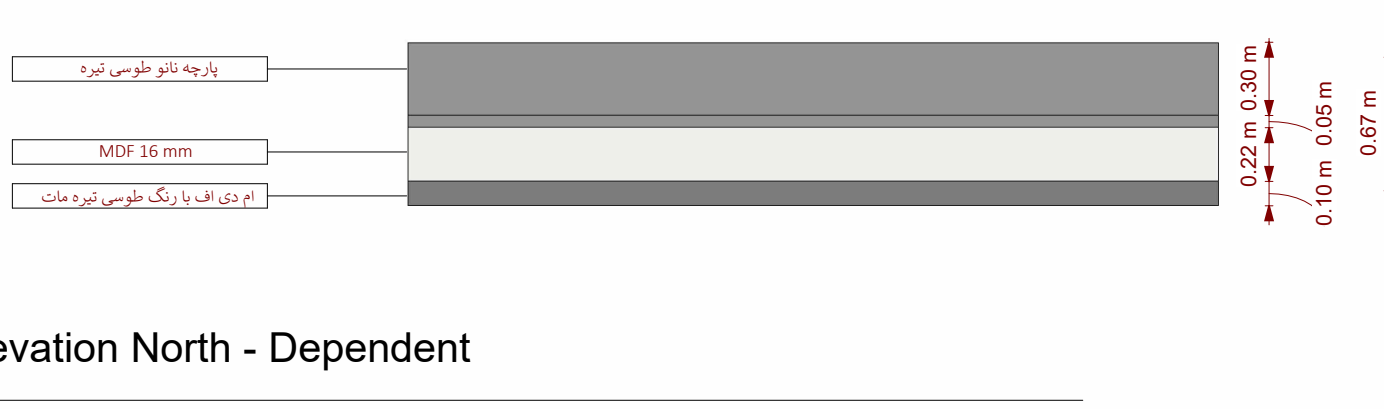

5 Elevation North - Dependent 1
1 : 20

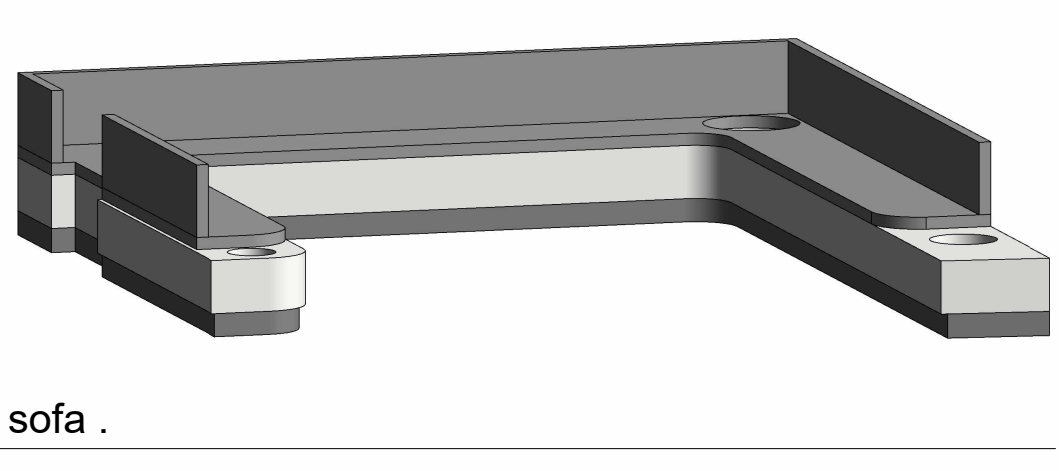

6 3d sofa .

مشخصات اجرا:

- روکش نشیمن و پشتی:پارچه نانو طوسی تیره
- نوع دوخت:دکمه دوزی
- فوم سرد با دانسیته بالا
- کلاف :ام دی اف
- بدنه :ام دی اف سوپر مات16 میلی متر
- پاخورام دی اف با رنگ طوسی تیره مات
- نورپردازی :ال ای دی خطی مخفی نچرال12 آمپر
- فضای زیر نشیمن به صورت باکس با درب لولایی ام دی اف و یراق آلات آرام بند

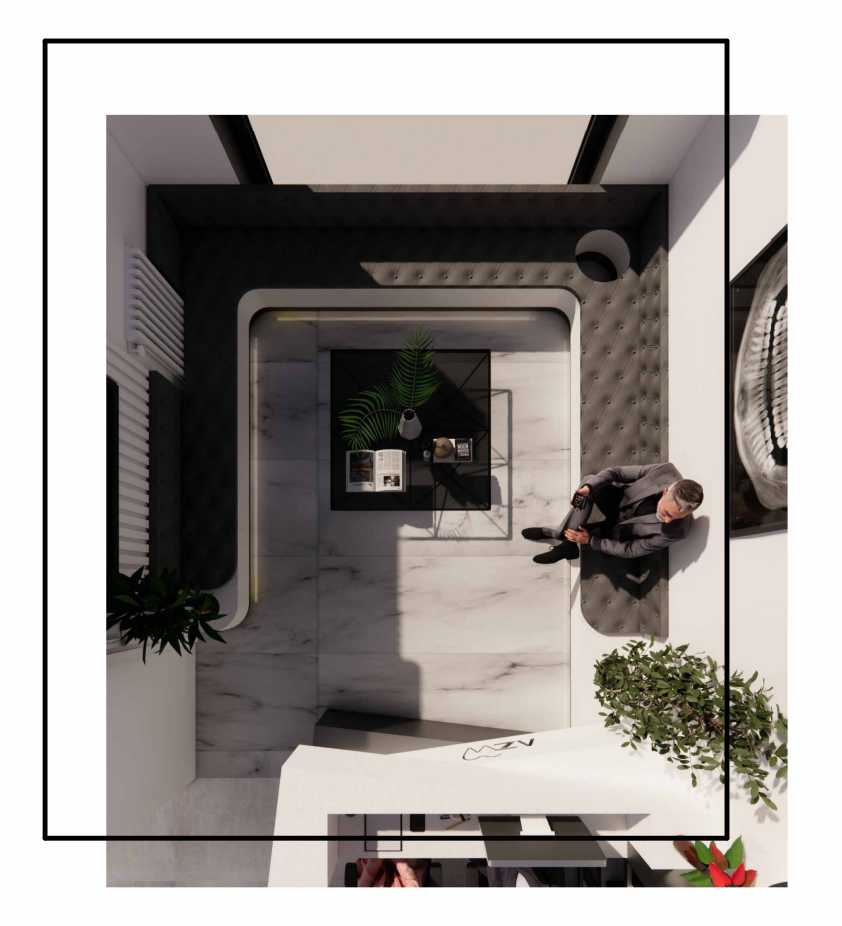

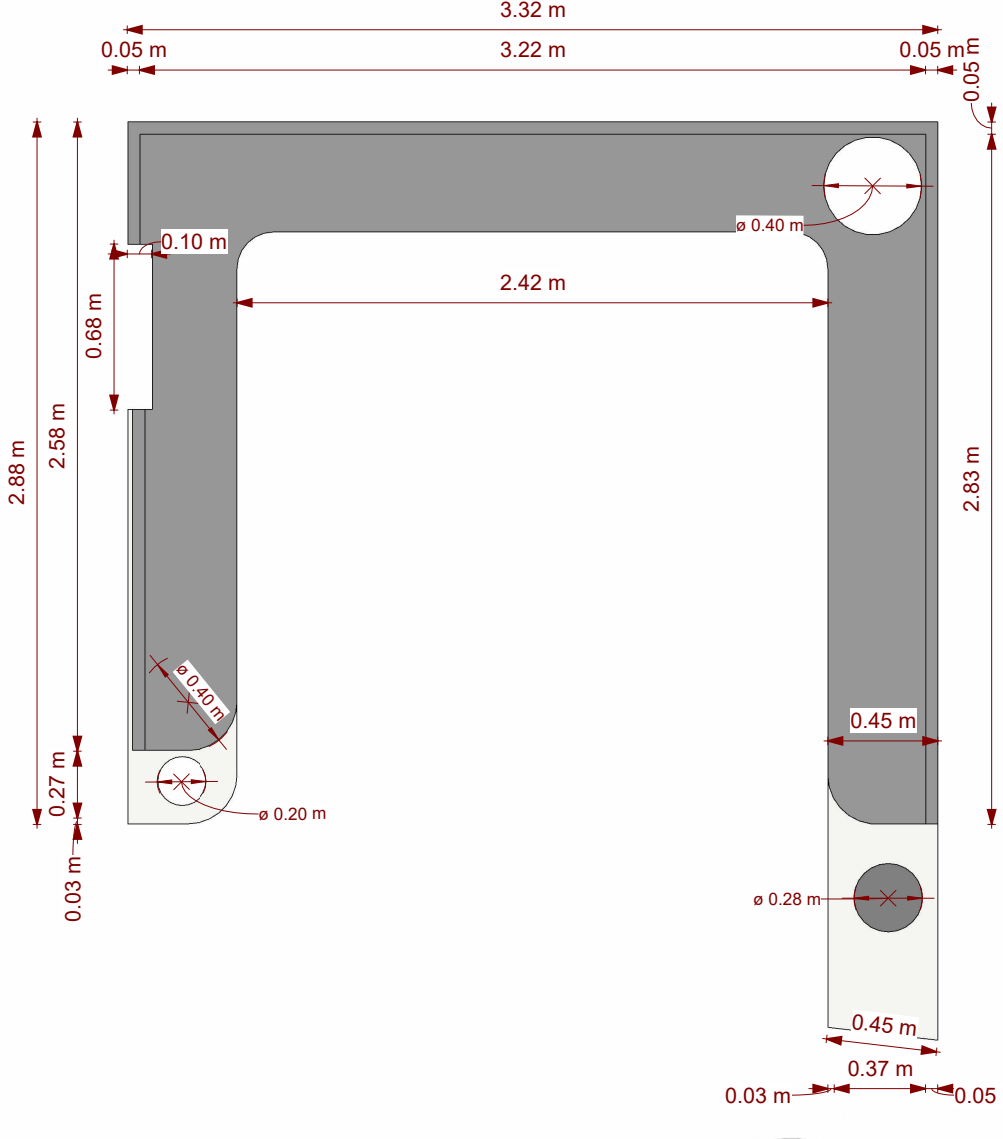

4 Dimention sofa - Dependent 1
1 : 20

Sahar
ARDESHIRNEZHAD
ARCHITECTURAL DESIGNER

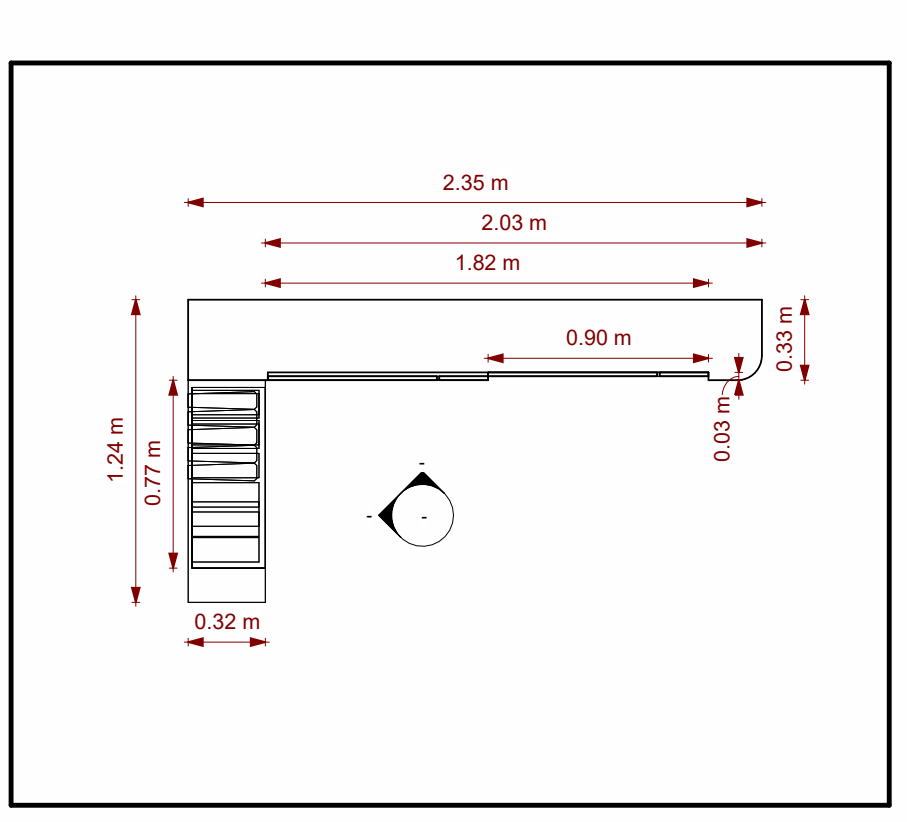

8 dimention komod
1 : 20

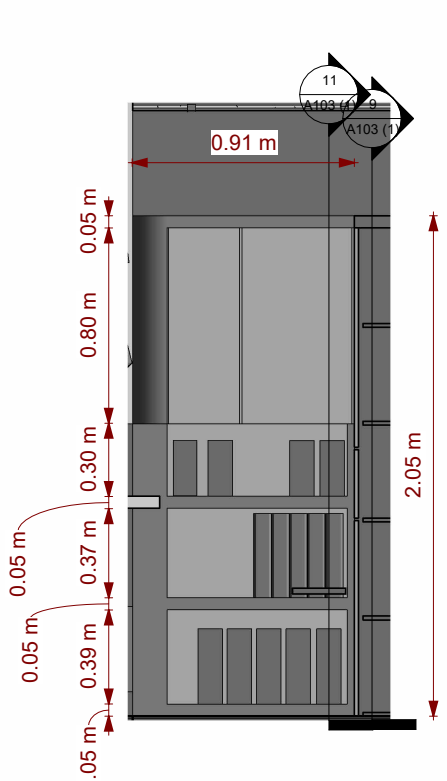

12 Section 3
1 : 20

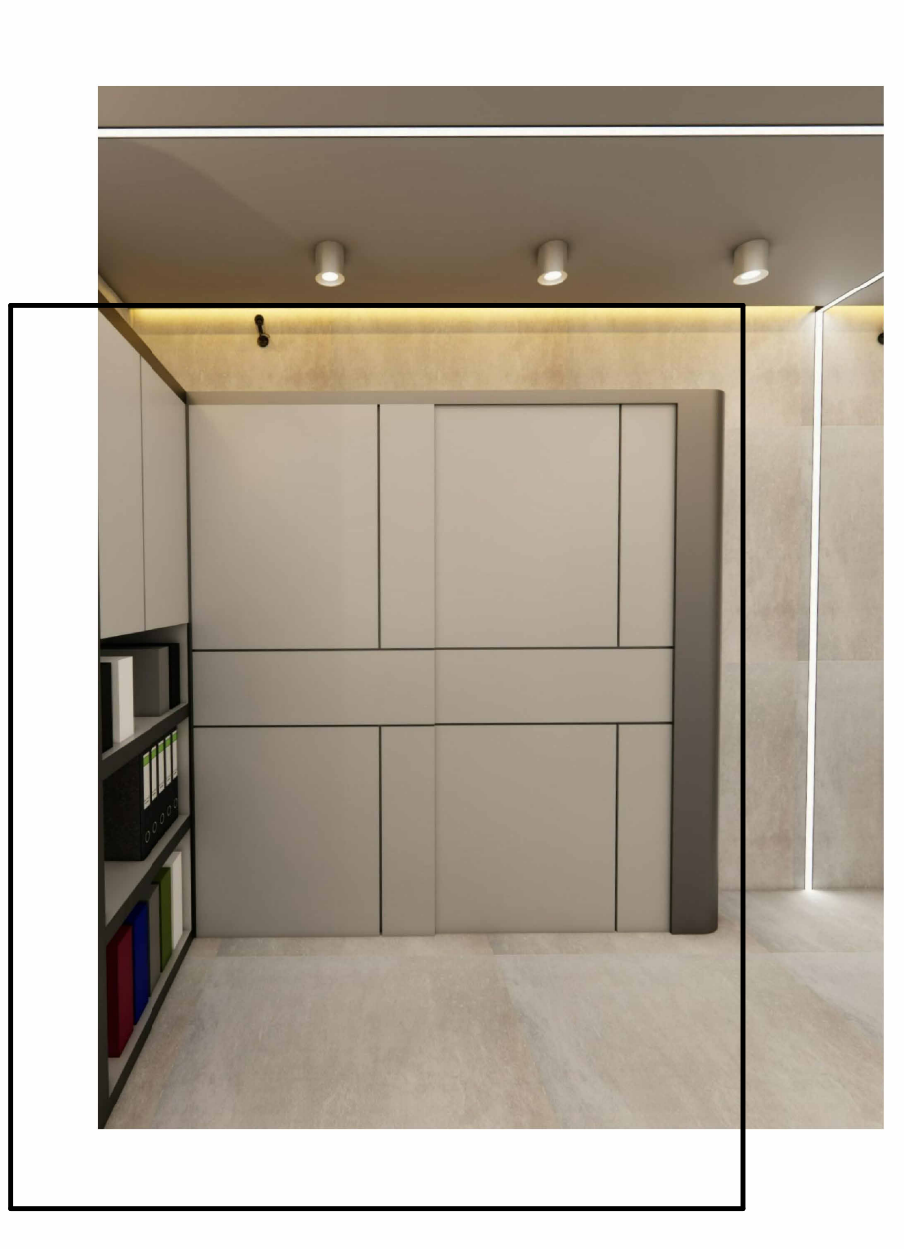

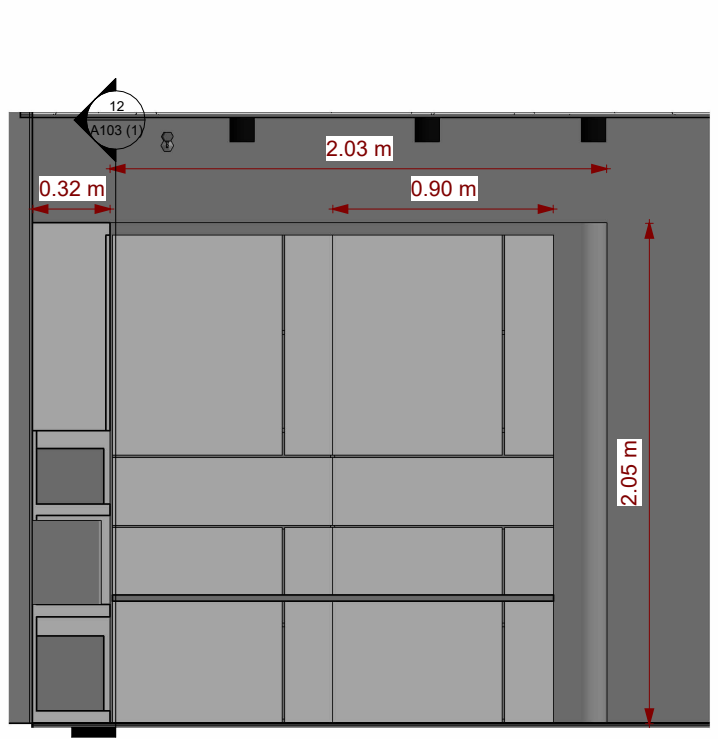

11 Section 2
1 : 20

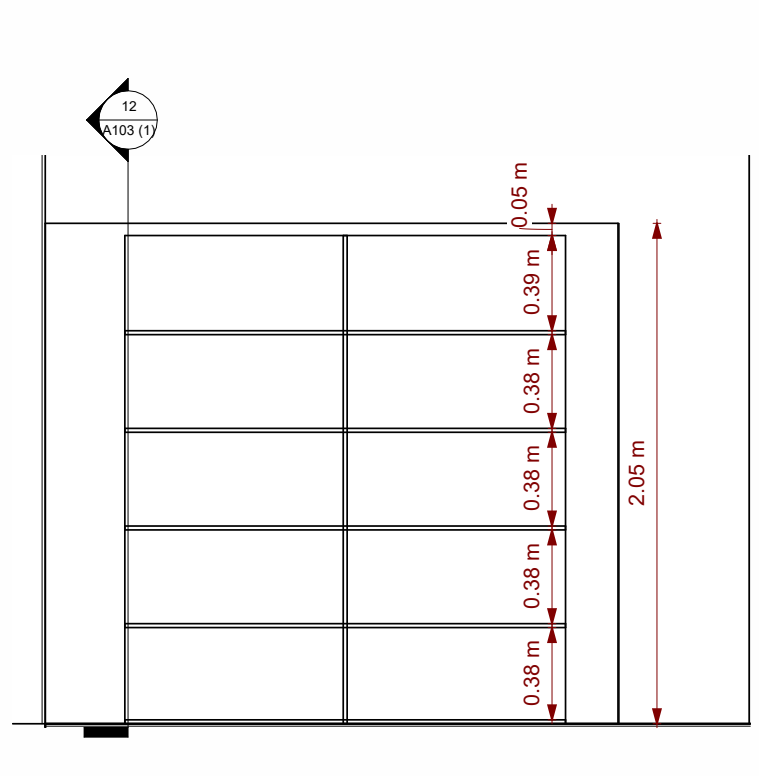

9 Section 4
1 : 20

Sahar
ARDESHIRNEZHAD
ARCHITECTURAL DESIGNER